

**SCALE NOTE**  
WRITTEN DIMENSIONS PERTAIN  
TO COORDINATE & VERIFY ALL  
DRAWING DIMENSIONS IN FIELD  
DURING CONSTRUCTION.  
NOTIFY THE  
RESIDENTIAL DESIGNER OF ANY  
DISCREPANCIES IMMEDIATELY  
BEFORE PROCEEDING

## WALL LEGEND

● Drainage	5.5" (2X5.5) STUD WALL + 5/8" DryWall on Both Faces
● Hot Water	5.5" (2X6) STUD WALL + 5/8" DryWall on Interior Face +2" Stucco Paint On Exterior Face
● Cold Water	5.5" (2X5.5) STUD WALL + 5/8" DryWall on Interior Face
	5.5" (2X5.5) STUD WALL + 2" Stucco Paint On Exterior Face
	7.25" (2X7.25) STUD WALL + 5/8" DryWall on Interior Face +2" Stucco Paint On Exterior Face
	3 1/2" (2X4) STUD WALL (COORDINATE WALL LOCATION W/ POCKET DOOR MANUFACTURER SHOP DRAWINGS)




1-3-2025



Level 1 - Dimensioned Floor Plan

Date:	1-3-2025	
Drawn By:	Author	
Job No.:		
#	Description	Date
1	Version 1	2024-10-21

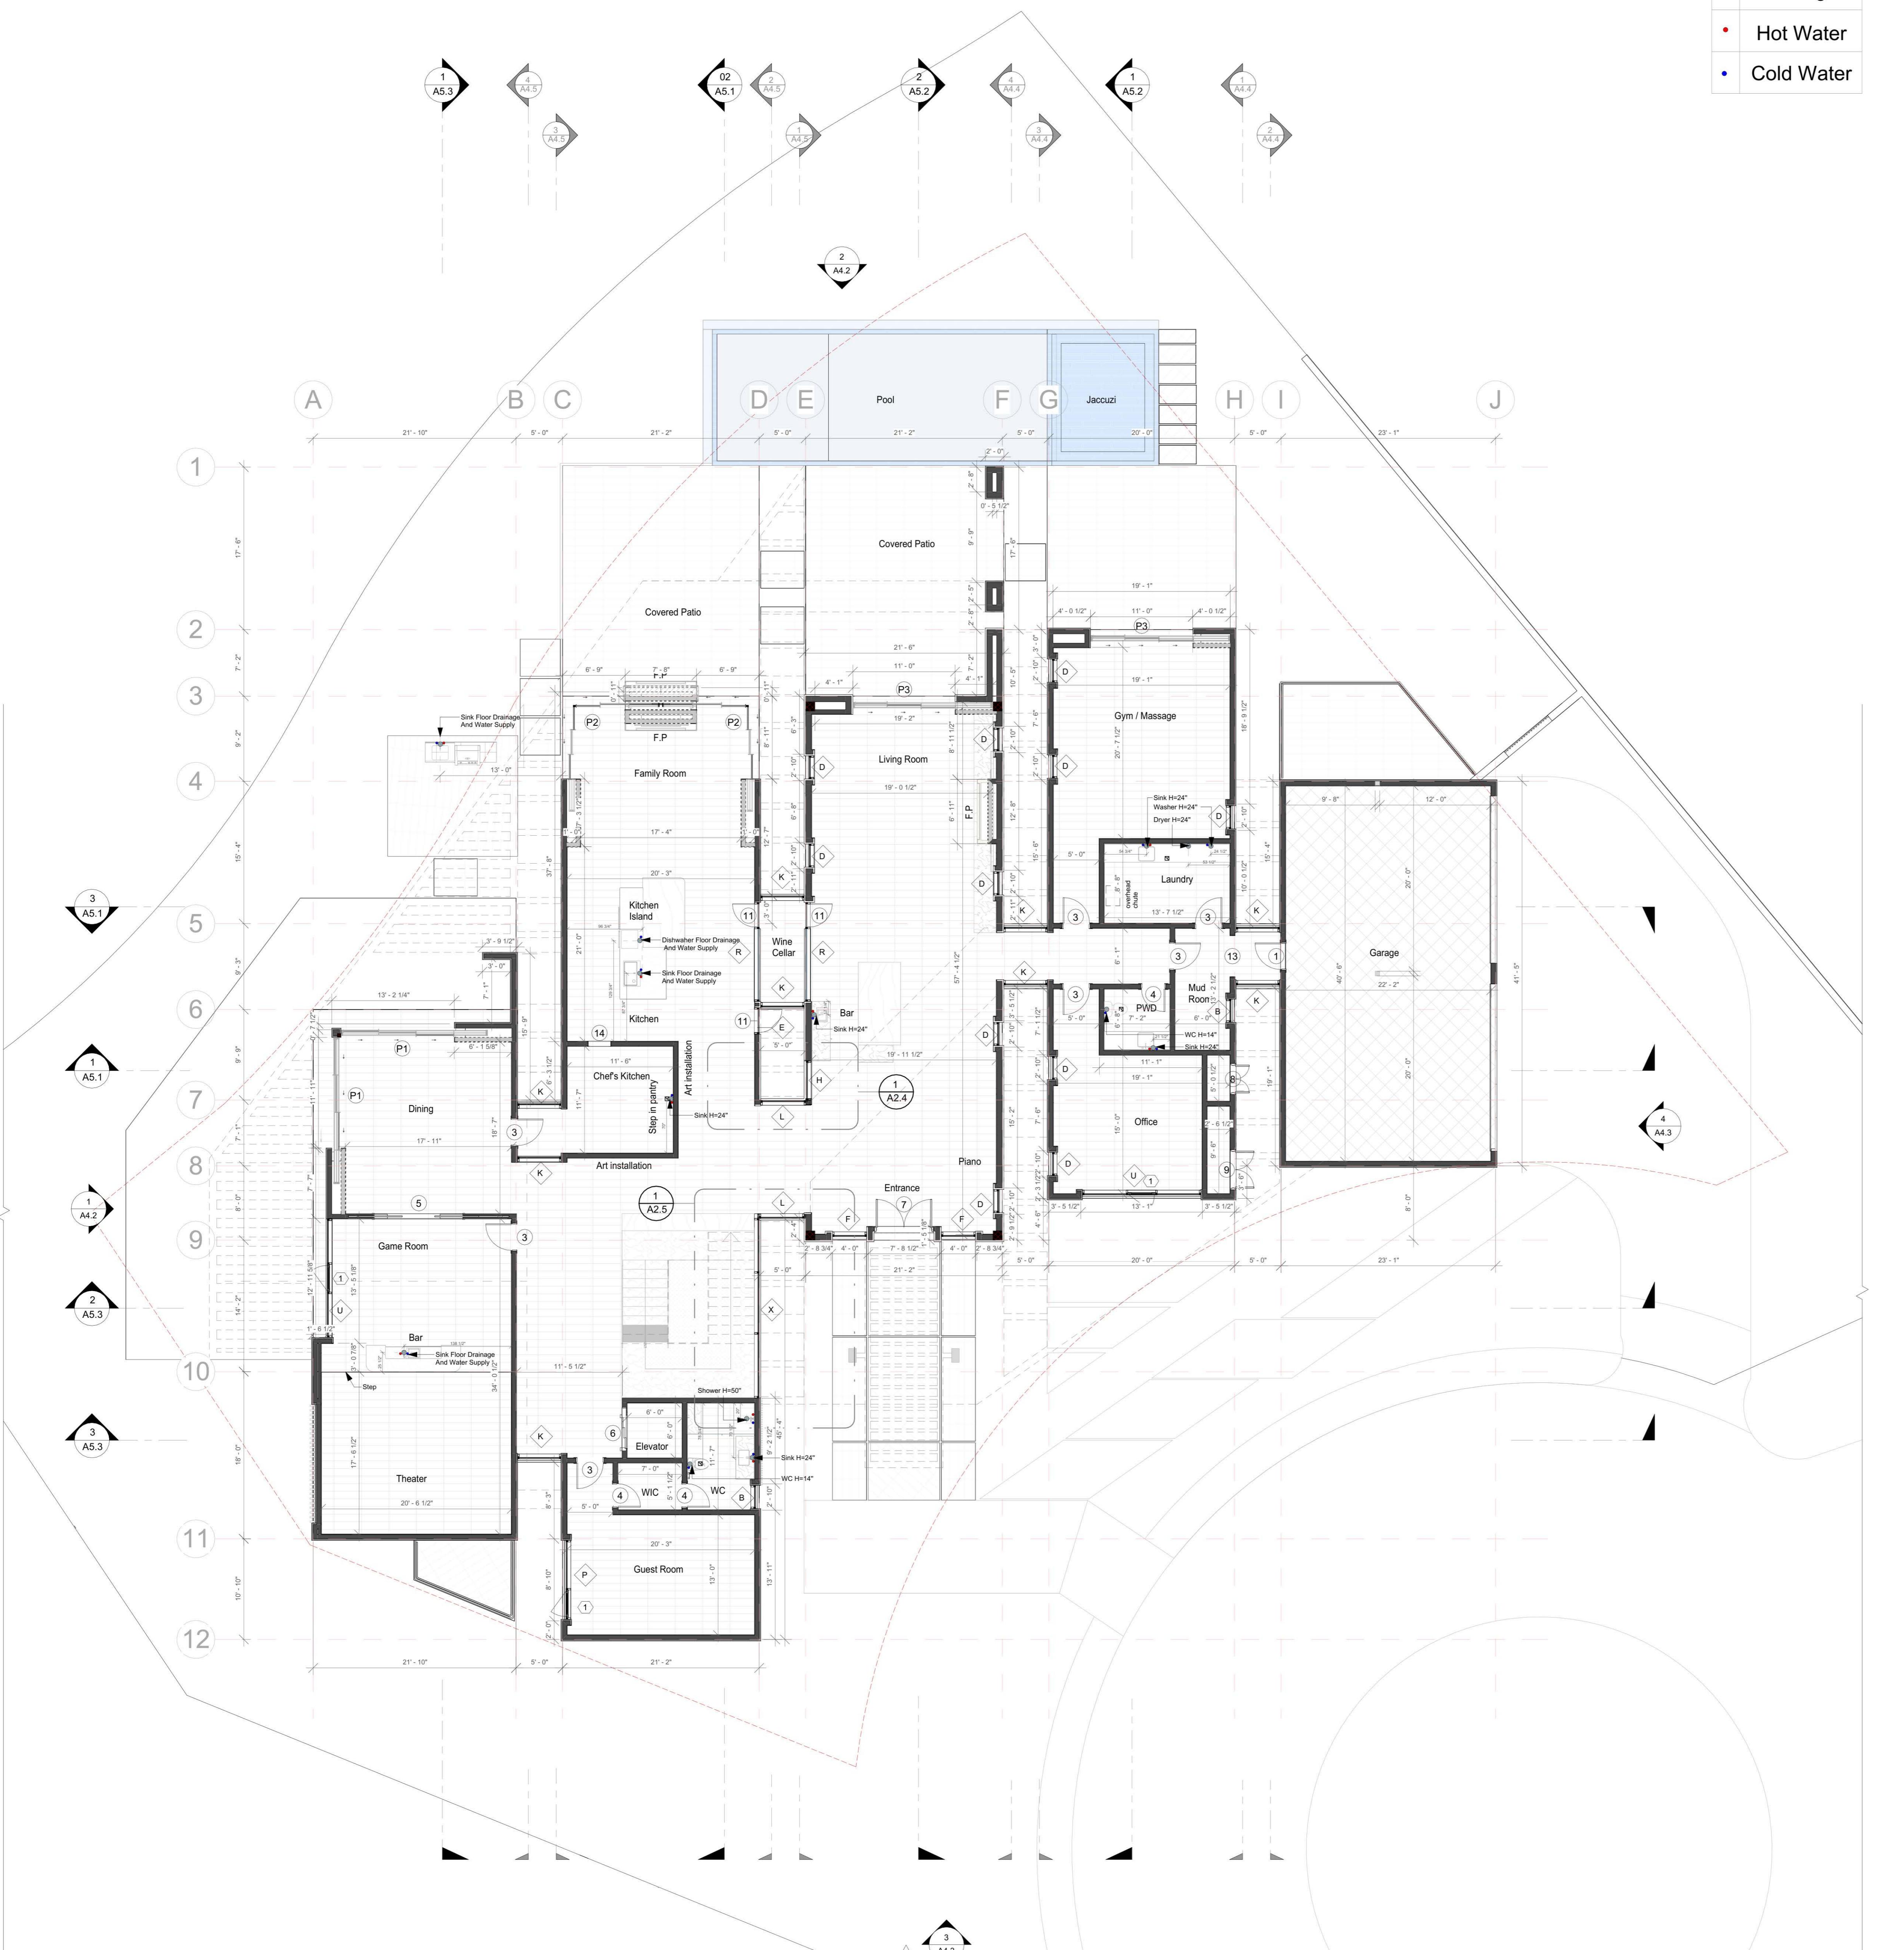

Level 1 - Dimensioned Floor Plan  
1/8" = 1'-0"

A2.0D