

ALL LEGEND

SCALE NOTE
TITTEN DIMENSIONS PRESIDE
ER SCALE. CONTRACTOR TO
ORDINATE & VERIFY ALL
AWING DIMENSIONS IN FIELD
DURING & PRIOR TO
NSTRUCTURE. NOTIFY THE
SIDENTIAL DESIGNER OF ANY
SCREPANCIES IMMEDIATELY
BEFORE PROCEEDING




1

1-3-2025



卷之三

A2.1D

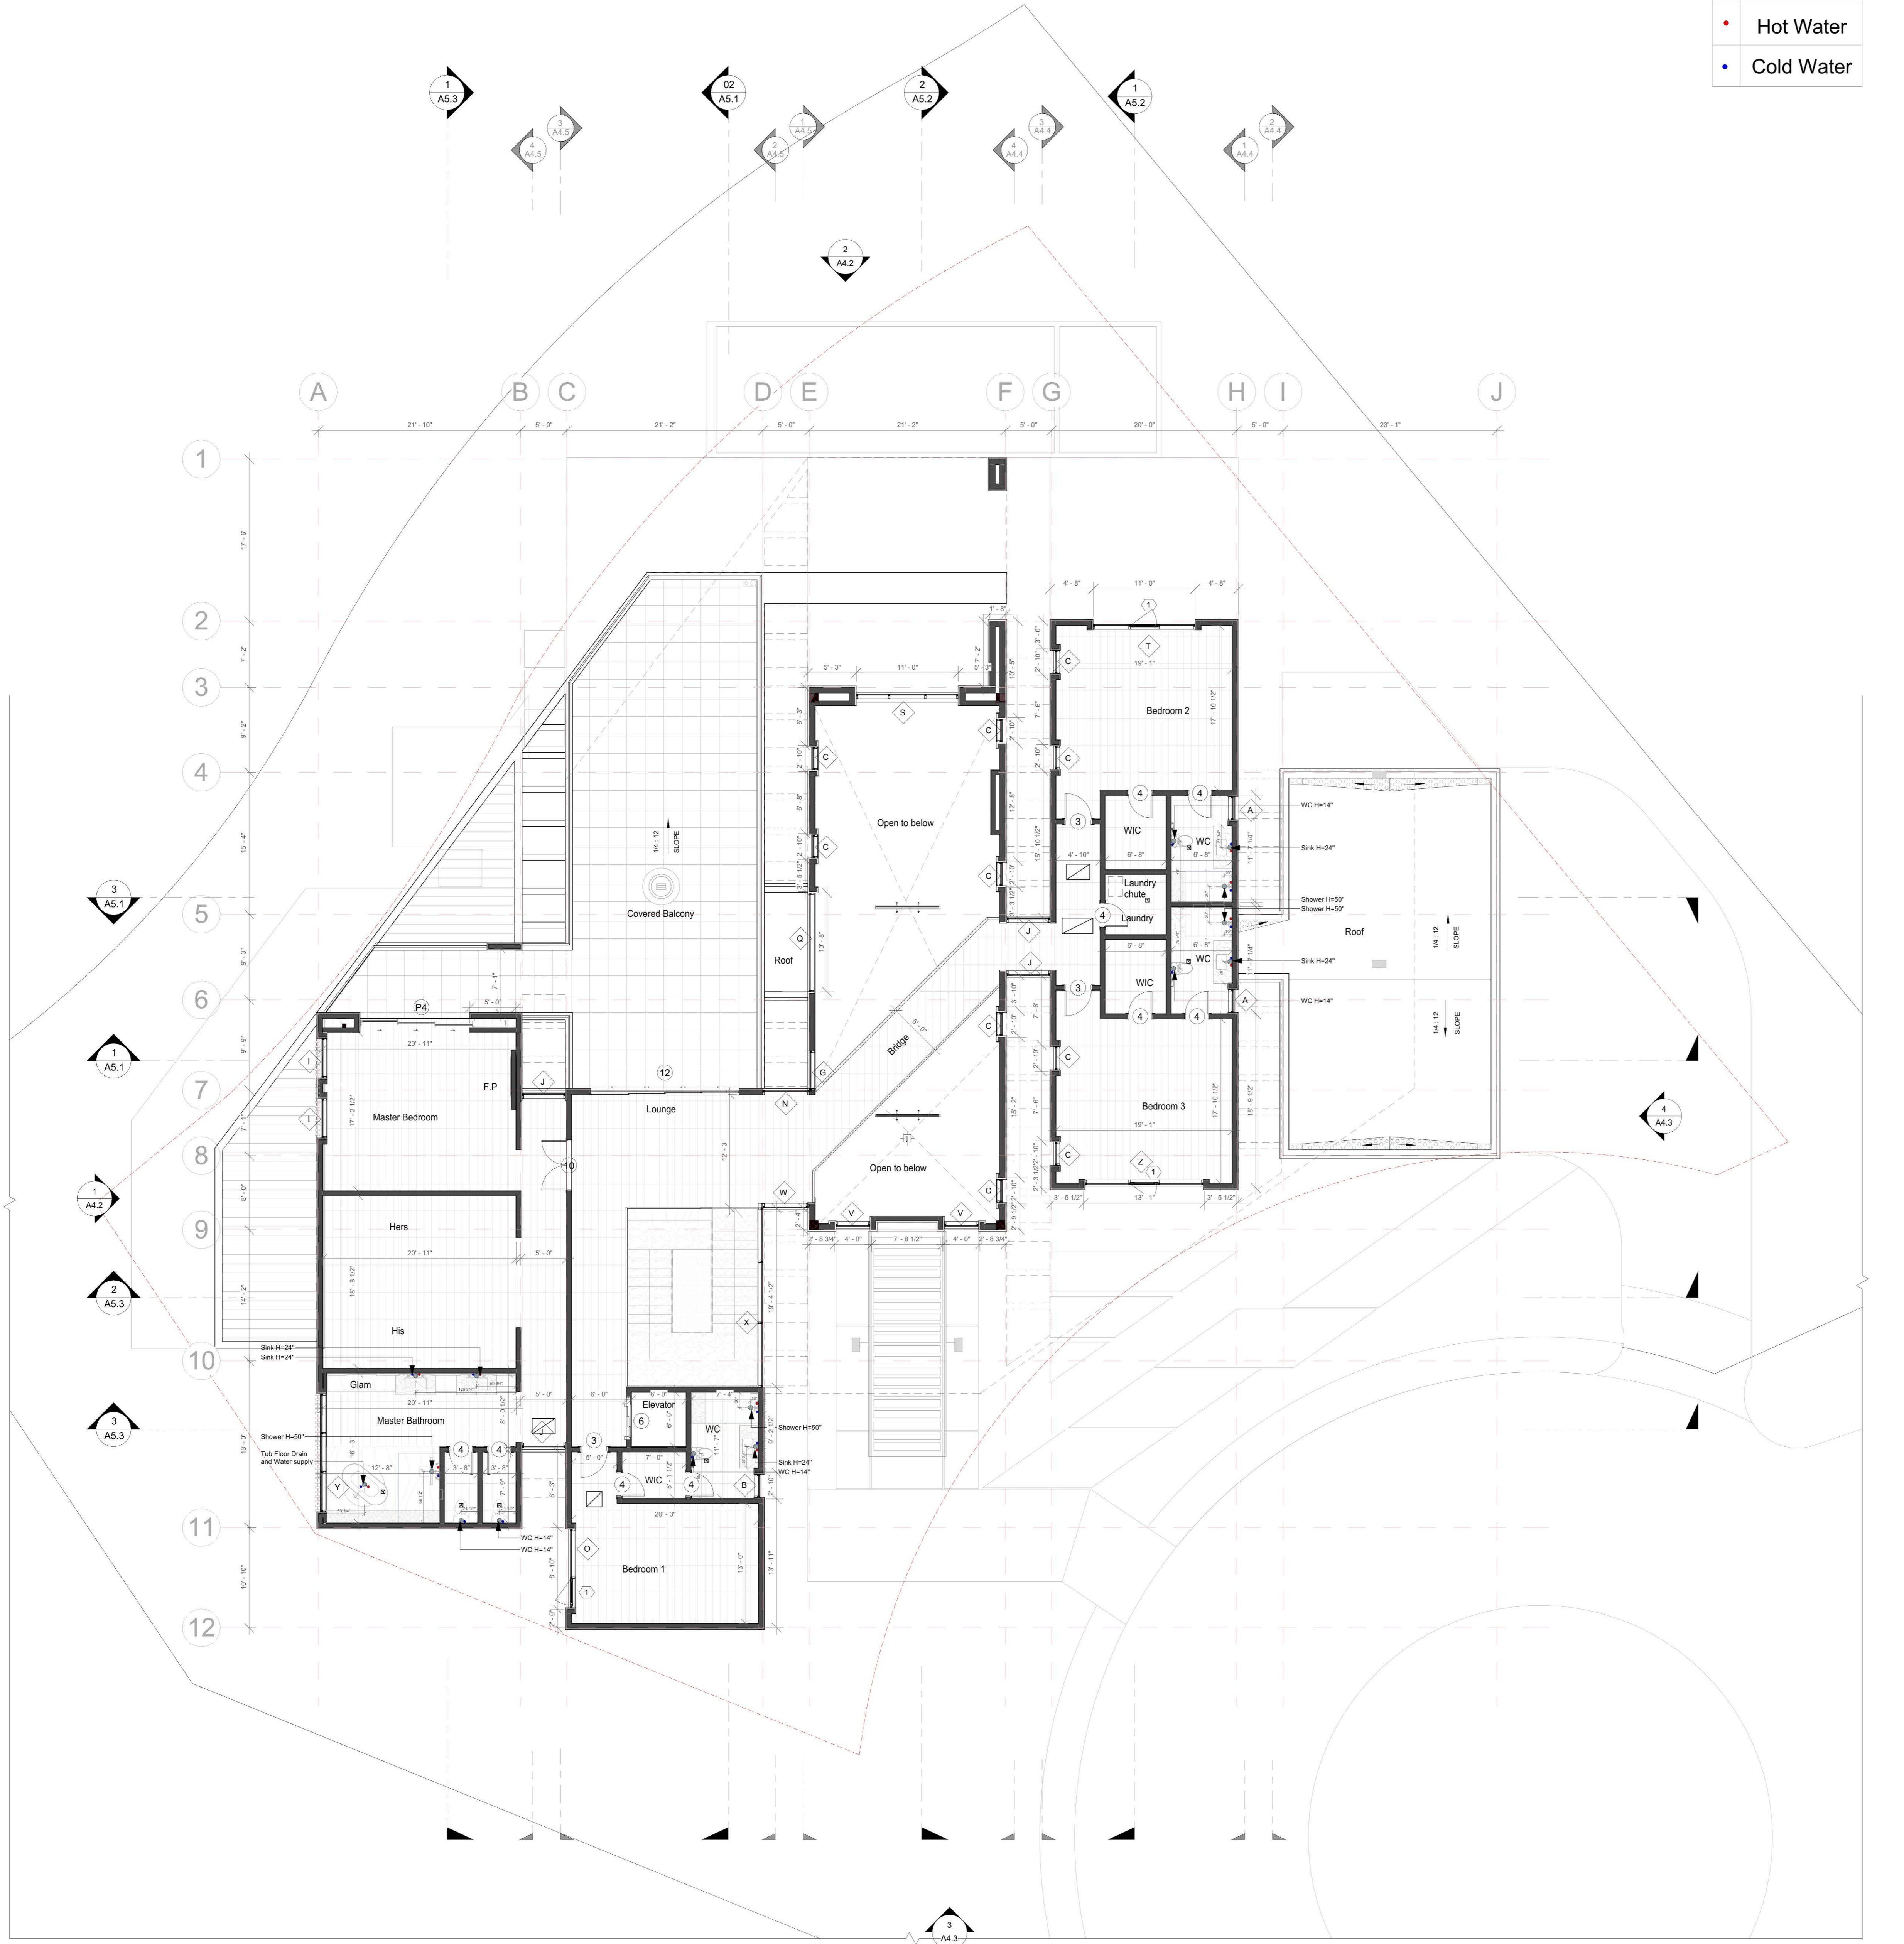

Level 2 - Dimensioned Floor Plan